



Aryan
architects and
interiors

•2D Plan Residential (G+3)

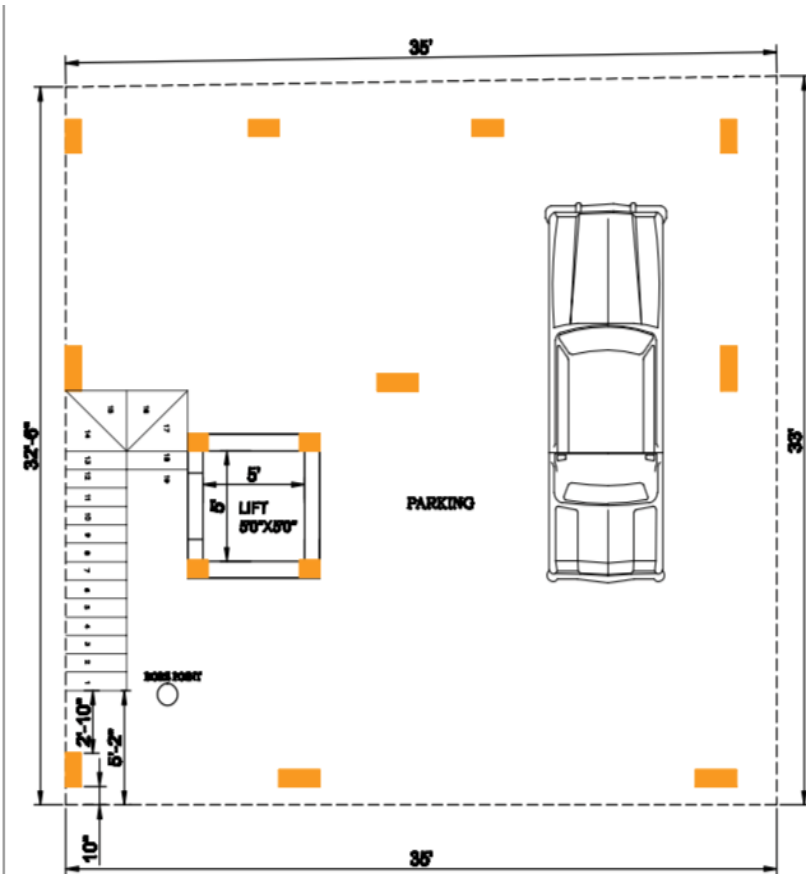

PROPOSED GROUND FLOOR PLAN

OPTION_04

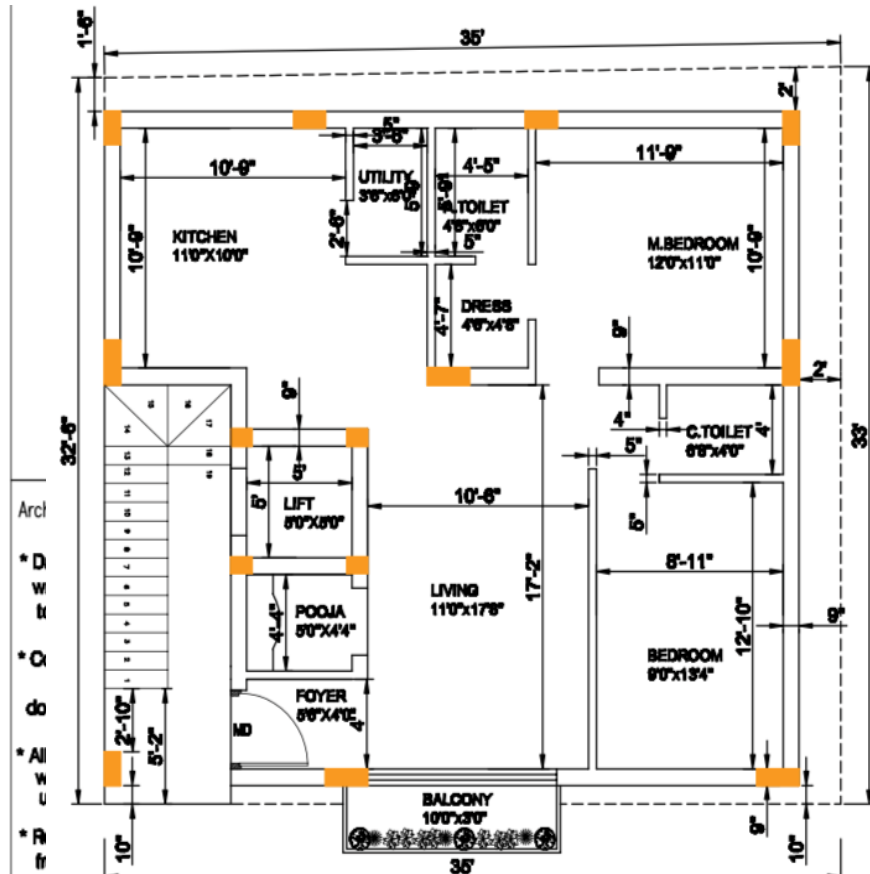


PROPOSED FIRST FLOOR PLAN

OPTION_04

Architect's instruction


- * Drawing not to be followed without written dimensions to be followed.
- * Contact the architect in case of doubts and discrepancies.
- * All walls are 6" thick, walls are 4" thick unless specified.
- * Roof Heights 10'-0" from Finished Floor.
- * All dimensions are in Feet & Inches.

DATE		DRG NO	PROJECT	TOTAL AREA	DATE		DRG NO	PROJECT	TOTAL AREA	ARCHITECT
DRAWN	BHM	AR-RC-04.	PROPOSED RESIDENCE FOR Mr.NARASIMHA MURTHY AT BANGALORE.	SQ FT	DRAWN	BHM	AR-RC-04.	PROPOSED RESIDENCE FOR Mr.NARASIMHA MURTHY AT BANGALORE.	SQ FT	ARYAN architect.
SCALE	NTS				SCALE	NTS				Ph: 9164640481

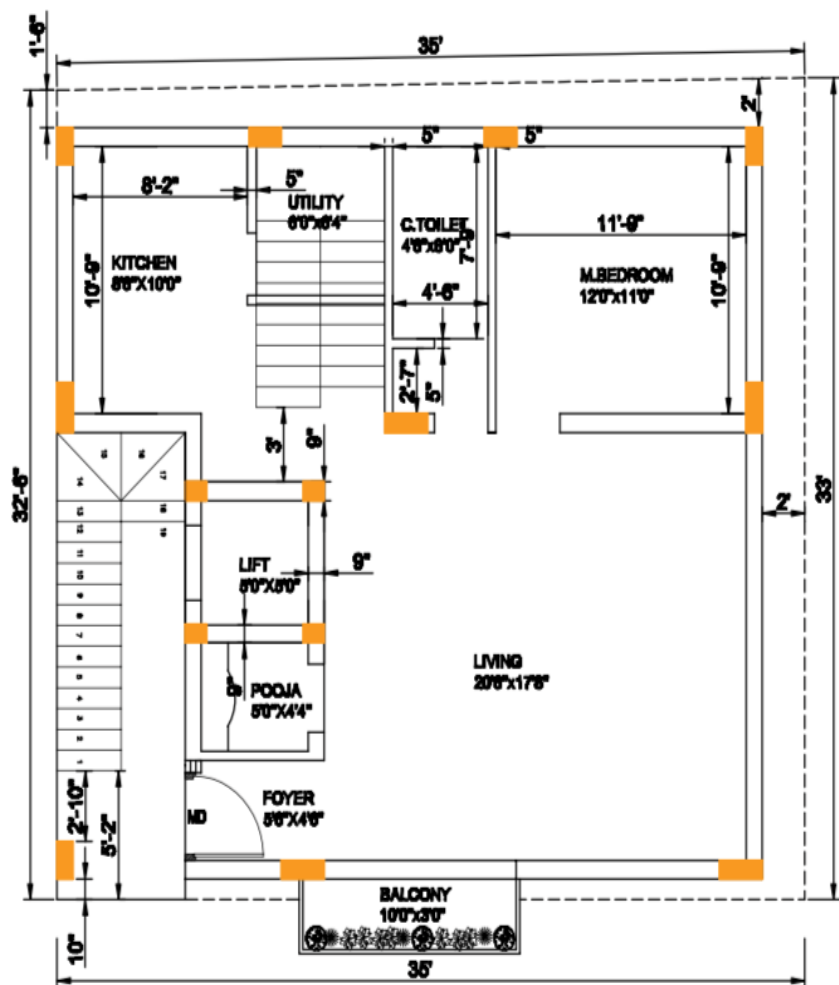

PROPOSED SECOND FLOOR PLAN

OPTION_04

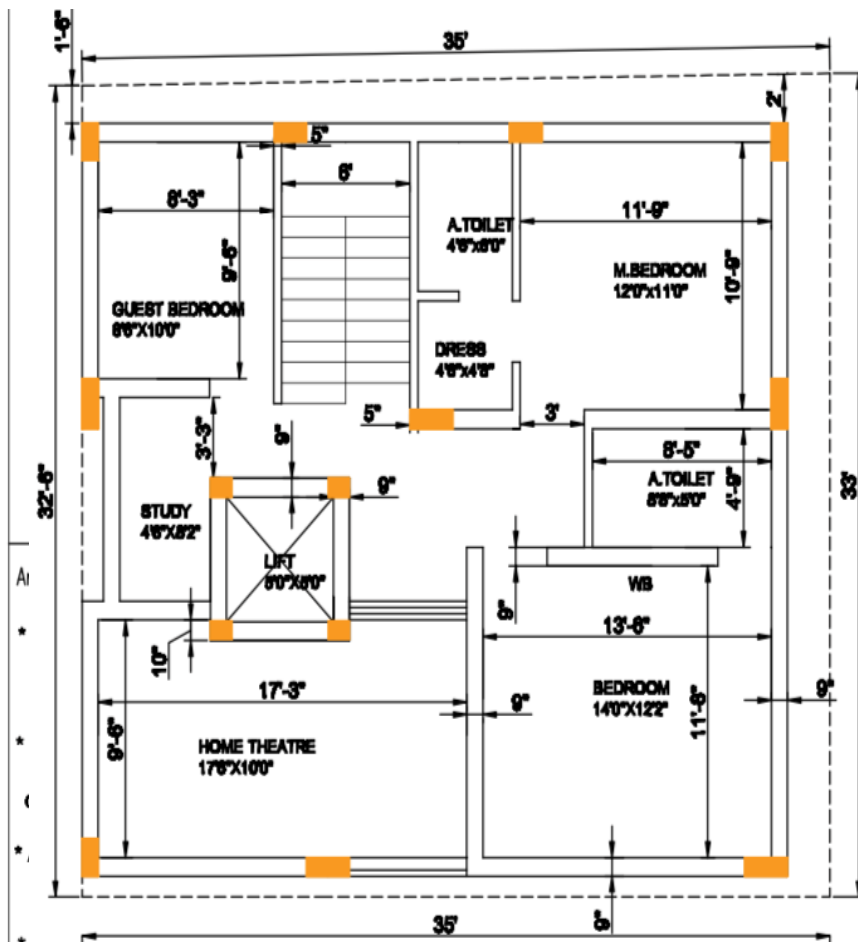

PROPOSED THIRD FLOOR PLAN

OPTION_04

Architect's instruction

* Drawing not to be scaled. All written dimensions are to be followed.

* Contact the architect in case of doubts and discrepancies.


* All walls are 6" thk. walls are 4" thk unless specified.

* Roof Heights 10'-0" from Finished Floor

* All dimensions are in Feet & Inches.

DATE		DRG NO	PROJECT	TOTAL AREA
DRAWN	BHM	AR-RC-04.	PROPOSED RESIDENCE FOR Mr.NARASIMHA MURTHY AT BANGALORE.	SQ FT
SCALE	NTS			

DATE		DRG NO	PROJECT	TOTAL AREA	ARCHITECT
DRAWN	BHM	AR-RC-04.	PROPOSED RESIDENCE FOR Mr.NARASIMHA MURTHY AT BANGALORE.	SQ FT	ARYAN architect
SCALE	NTS				Ph: 9184640481

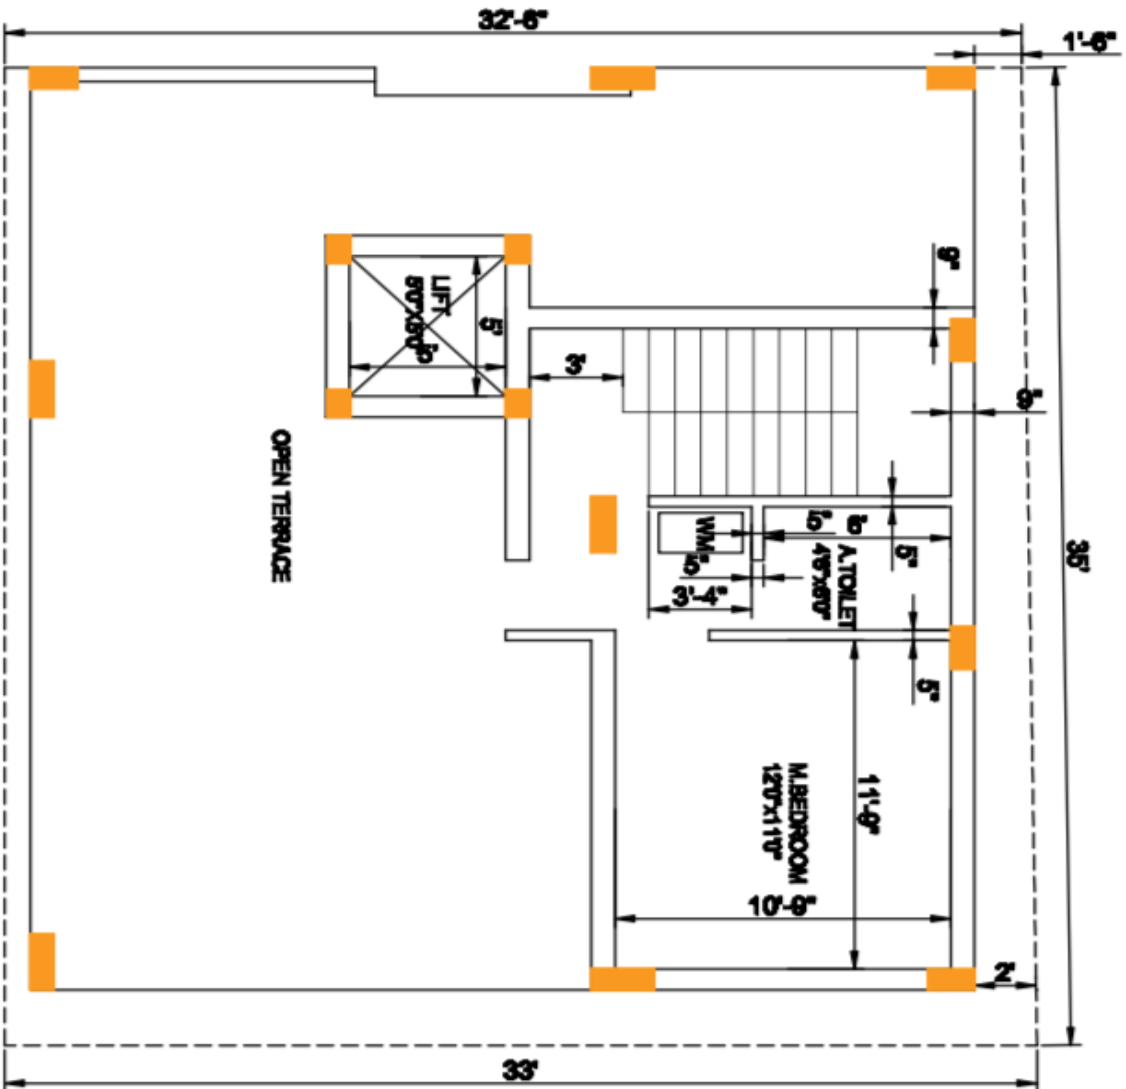

PROPOSED TERRACE FLOOR PLAN

OPTION_04

DATE	DRG NO	PROJECT	TOTAL AREA	ARCHITECT
DRAWN	BHM	AR-RC-04.	PROPOSED RESIDENCE FOR MR.NARASIMHA MURTHY AT BANGALORE.	ARYAN archite
SCALE	NTS		SO FT	Ph: 916464048

Architect's instructio

* Drawing not to be
written dimensions
to be followed.

* Contact the archite
in case of
doubts and discrep

* All walls are 6" thk
walls are 4" thk
unless specified.

* Roof Heights 10'-0"
from Finished Floo

* All dimensions are
in Feet & inches.

• Front Elevation (G+2)



• Front Elevation Commercial (G+3)



• Front Elevation G+2



• Front Elevation (G+1)



• Interior View of Living



• Interior View of Living



• Interior View of Dining



• Interior view of Foyer



- Interior view of Foyer




• Interior view of Kitchen



• Interior view of Master Bedroom



• Interior view of Master Bedroom

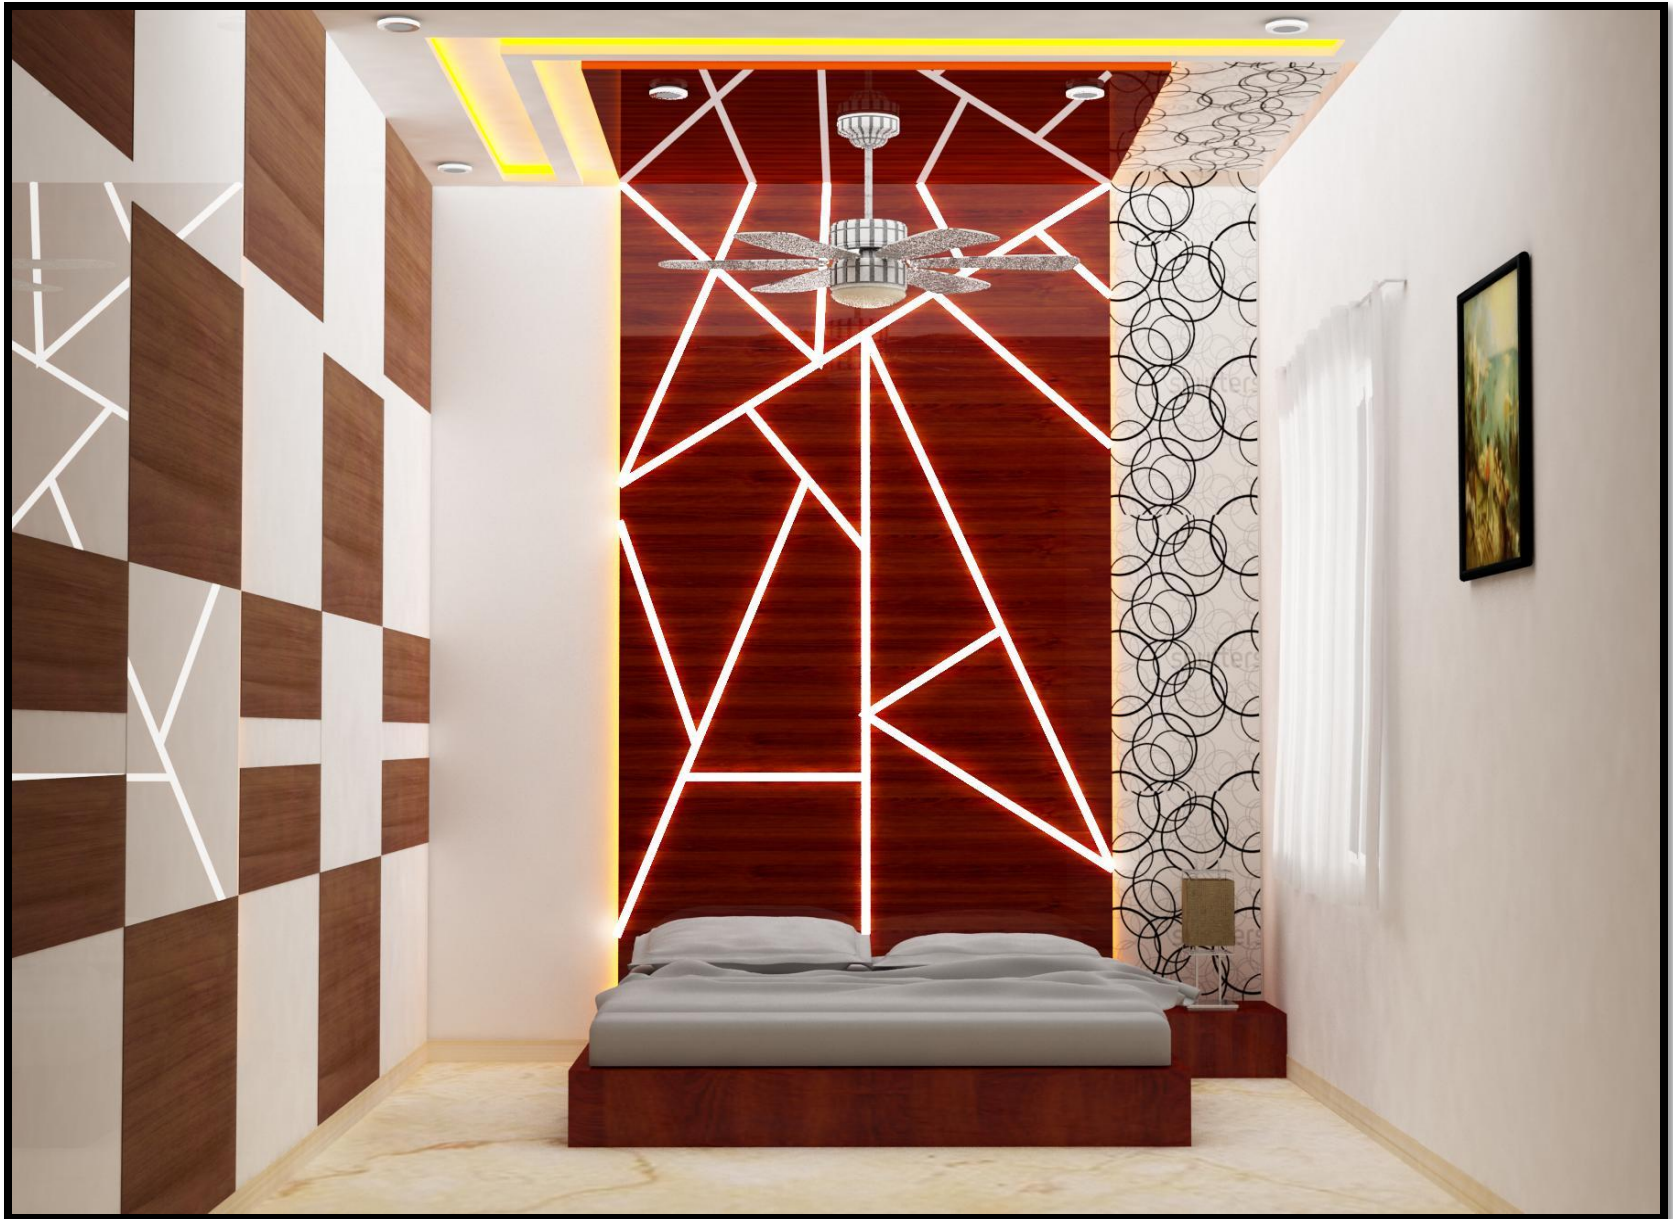

• Interior view of Bedroom




• Interior view of Bedroom



• Interior view of Double Height



• Interior view of Double Height

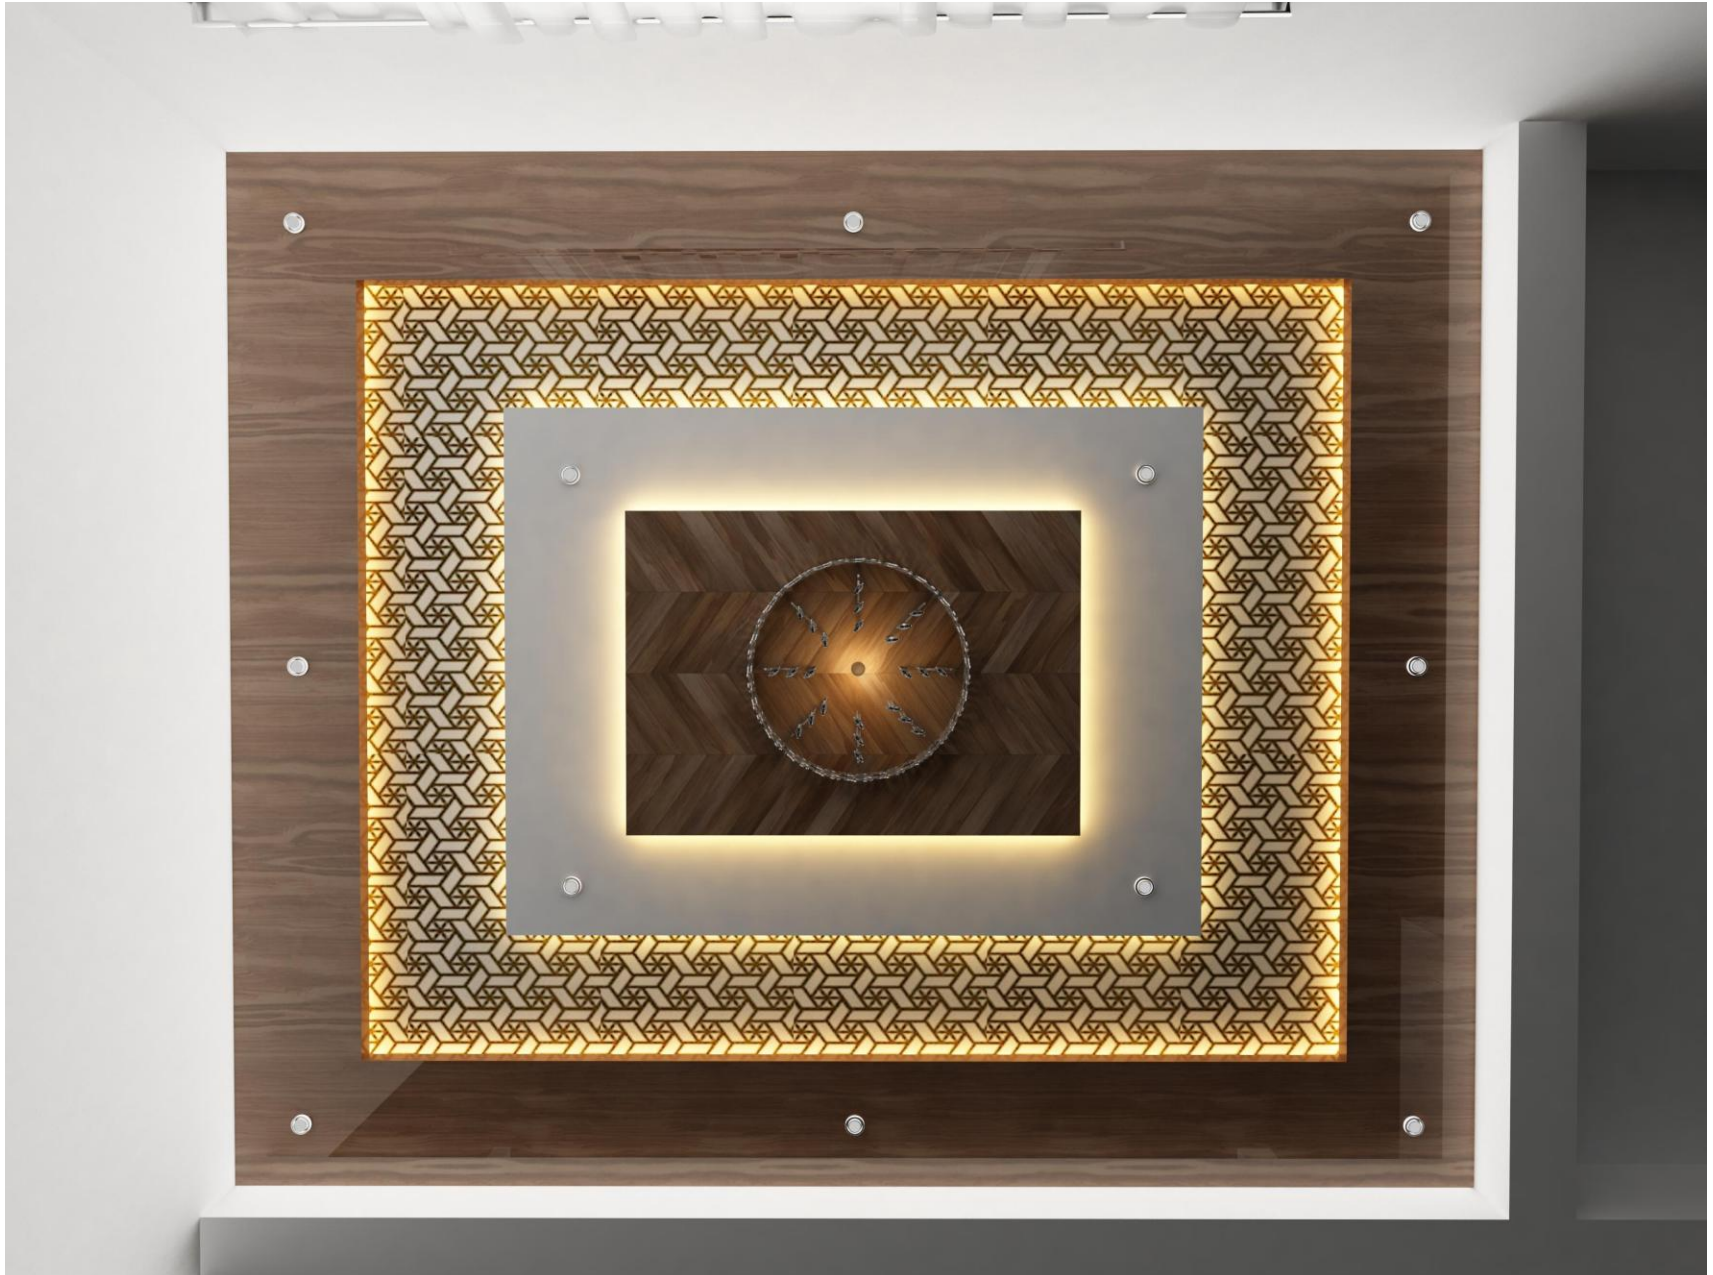

• Interior view of Bathroom



• Interior view of Balcony



•Side view of Balcony



• Interior view of GYM



THANKING
YOU